
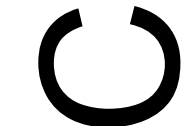


These drawings represent design and conceptual information only. They do not address the structural or electrical appropriateness of the design's installation and realization. All applicable fire and safety codes are to be strictly applied.

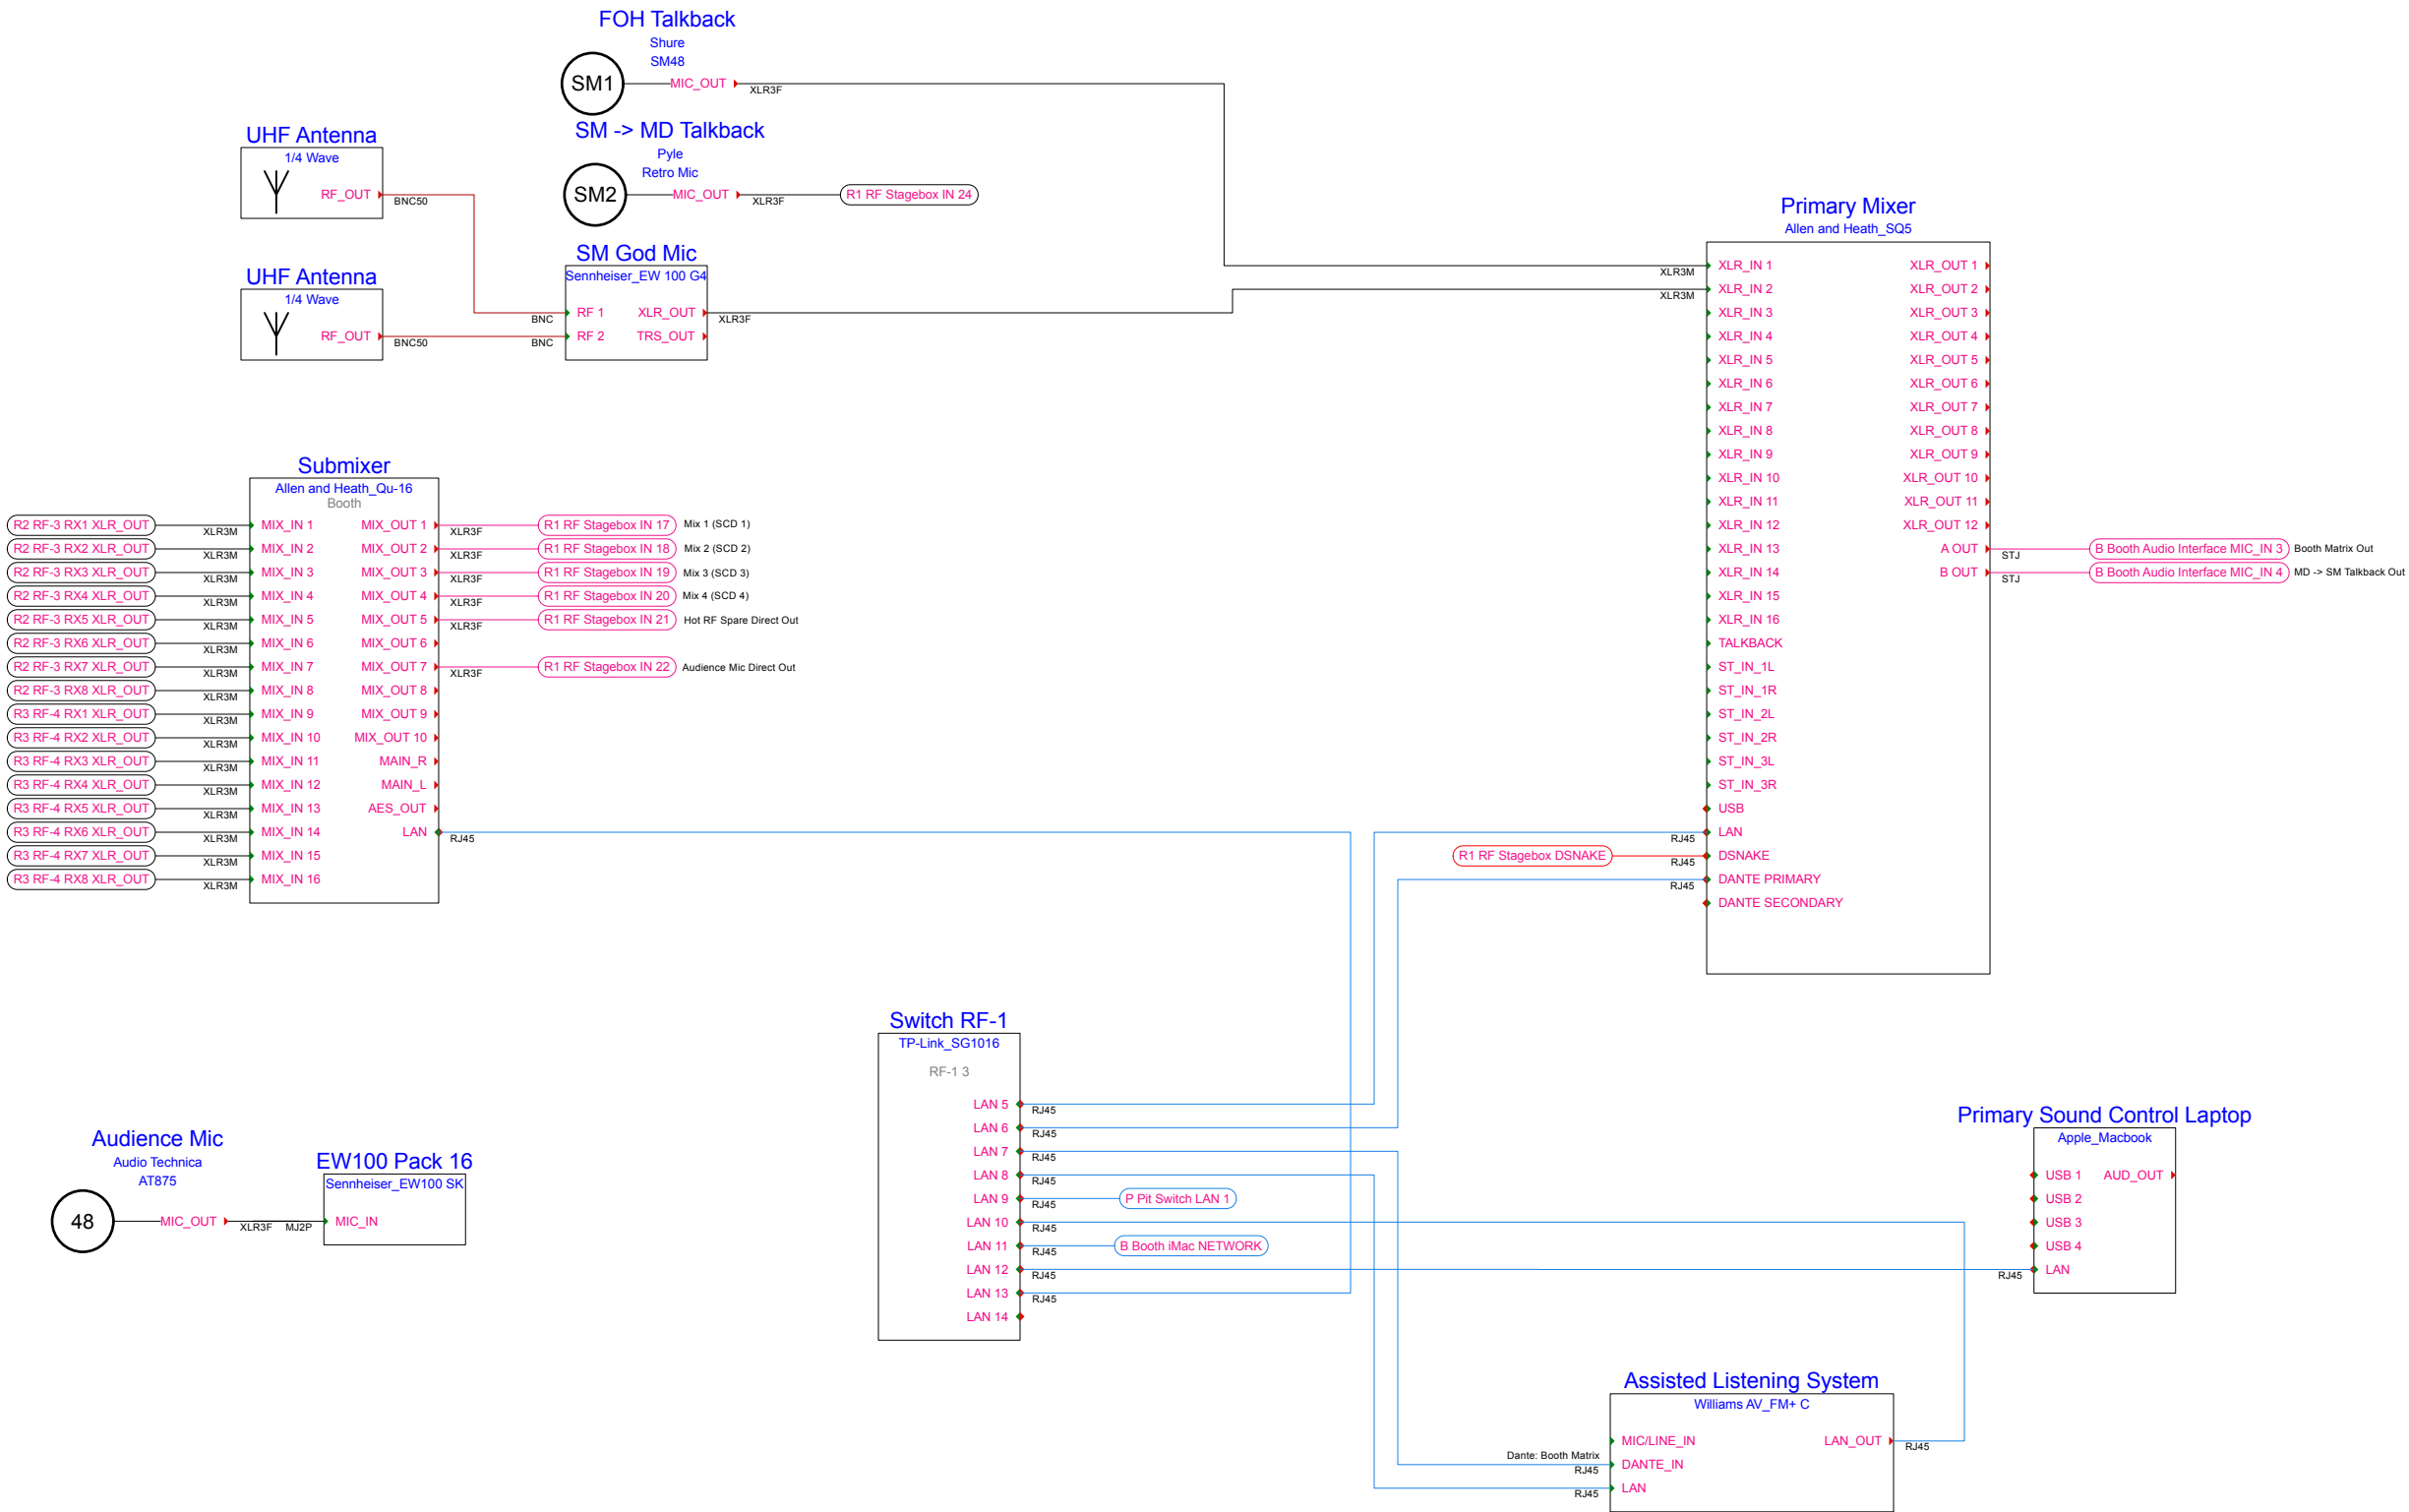

Audio System Core

"THE HUNCHBACK OF NOTRE DAME"

GEORGE FOX UNIVERSITY THEATRE - WOOD-MAR AUDITORIUM




PLATE:

SCALE:
DATE:
REV:
PAPER SIZE: 11" x 17"

DIRECTOR: BEN TISSELL
SOUND DESIGNER: TODD RYLAARSDAM

VECTORWORKS EDUCATIONAL VERSION

These drawings represent design and conceptual information only. They do not address the structural or electrical appropriateness of the design's installation and realization. All applicable fire and safety codes are to be strictly applied.

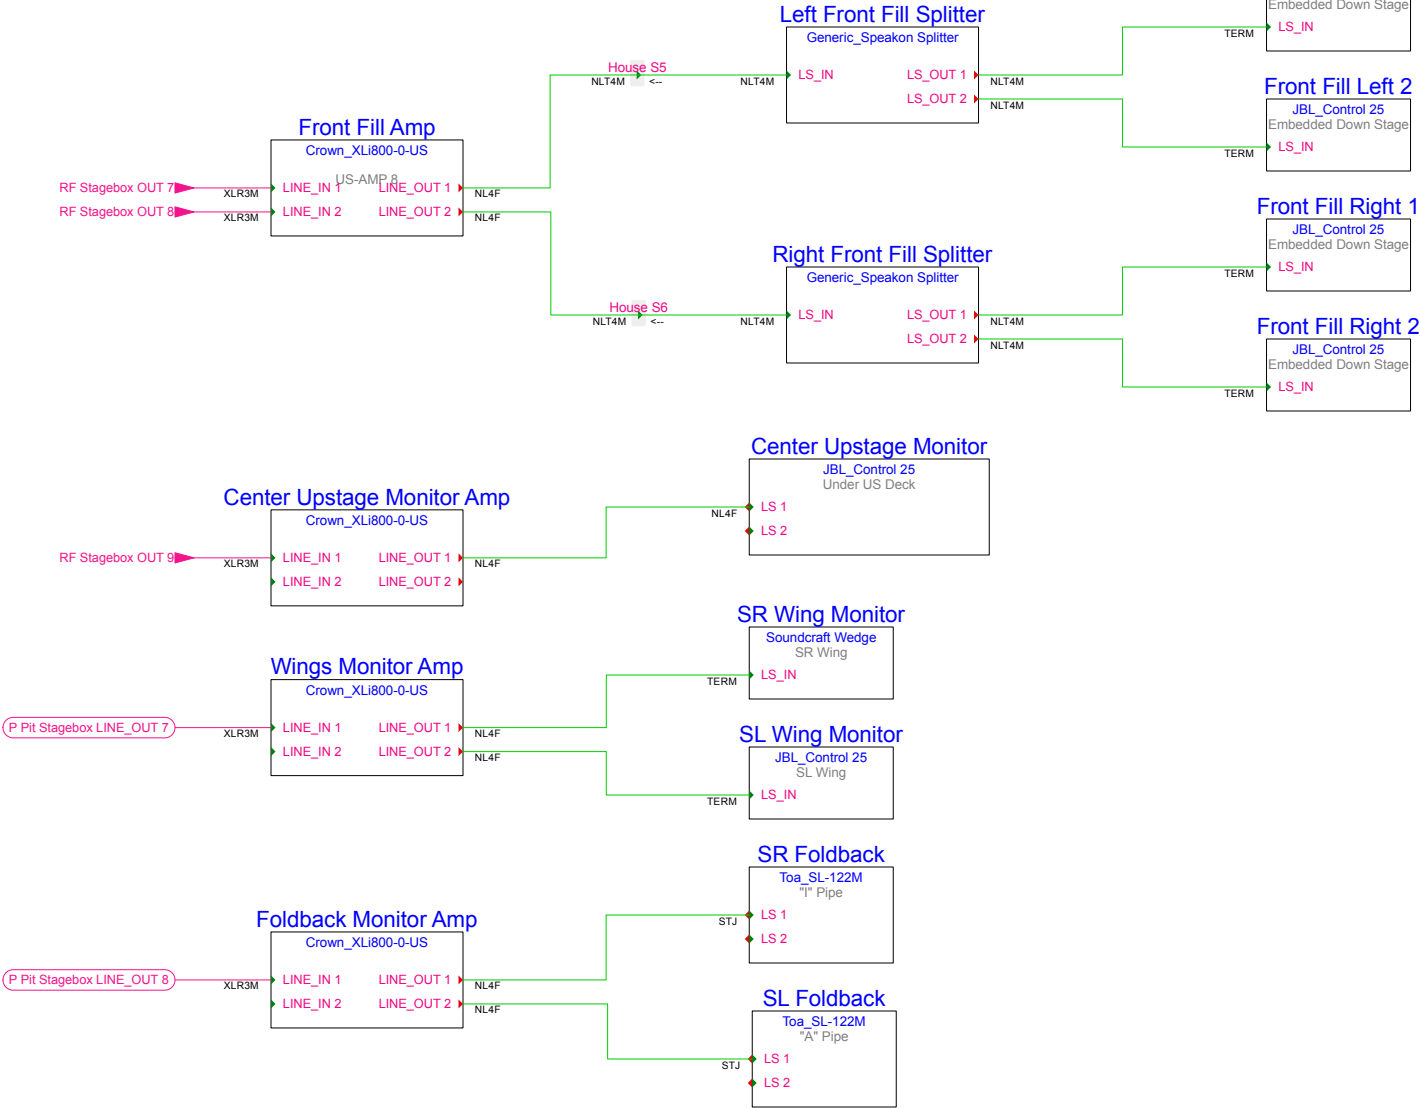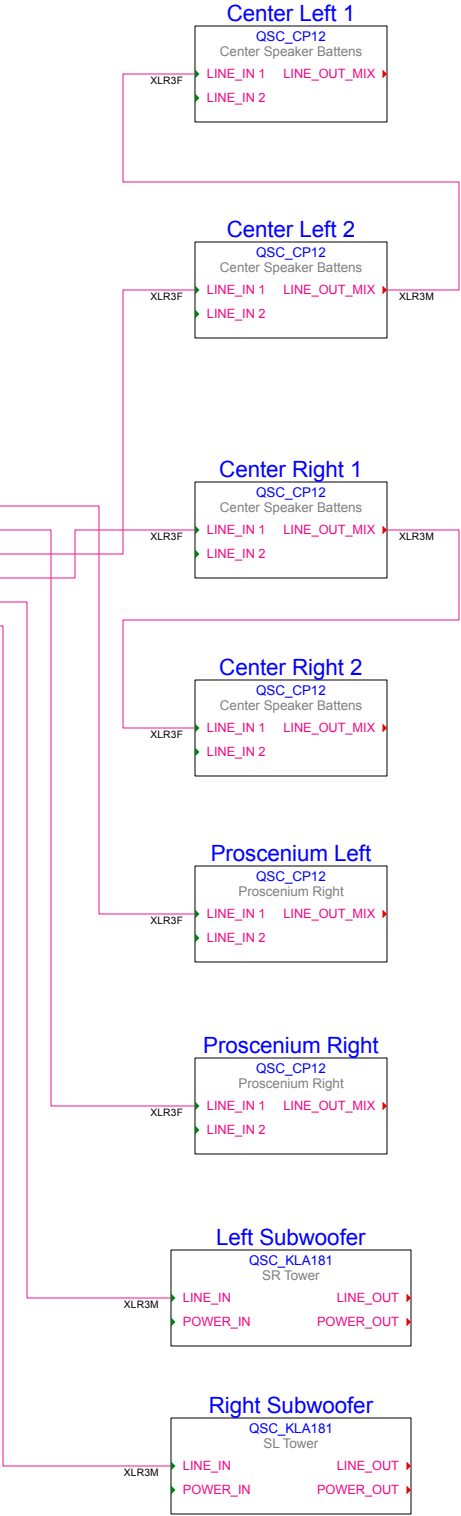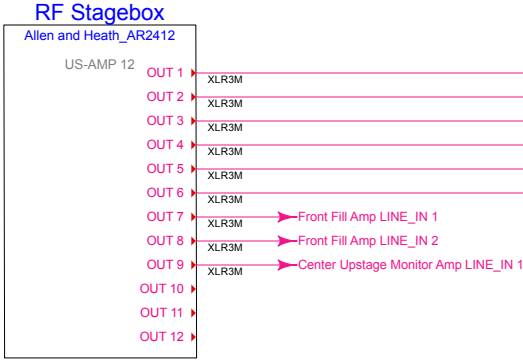

VECTORWORKS EDUCATIONAL VERSION

VECTORWORKS EDUCATIONAL VERSION

GEORGE FOX UNIVERSITY THEATRE - WOOD-MAR AUDITORIUM

"THE HUNCHBACK OF NOTRE DAME"

Speakers and Amplifiers

PLATE:


SCALE:
DATE:
REV:
PAPER SIZE: 11" x 17"

DIRECTOR: BEN TISSELL
SOUND DESIGNER: TODD RYLAARSDAM



S

These drawings represent design and conceptual information only. They do not address the structural or electrical appropriateness of the design's installation and realization. All applicable fire and safety codes are to be strictly applied.

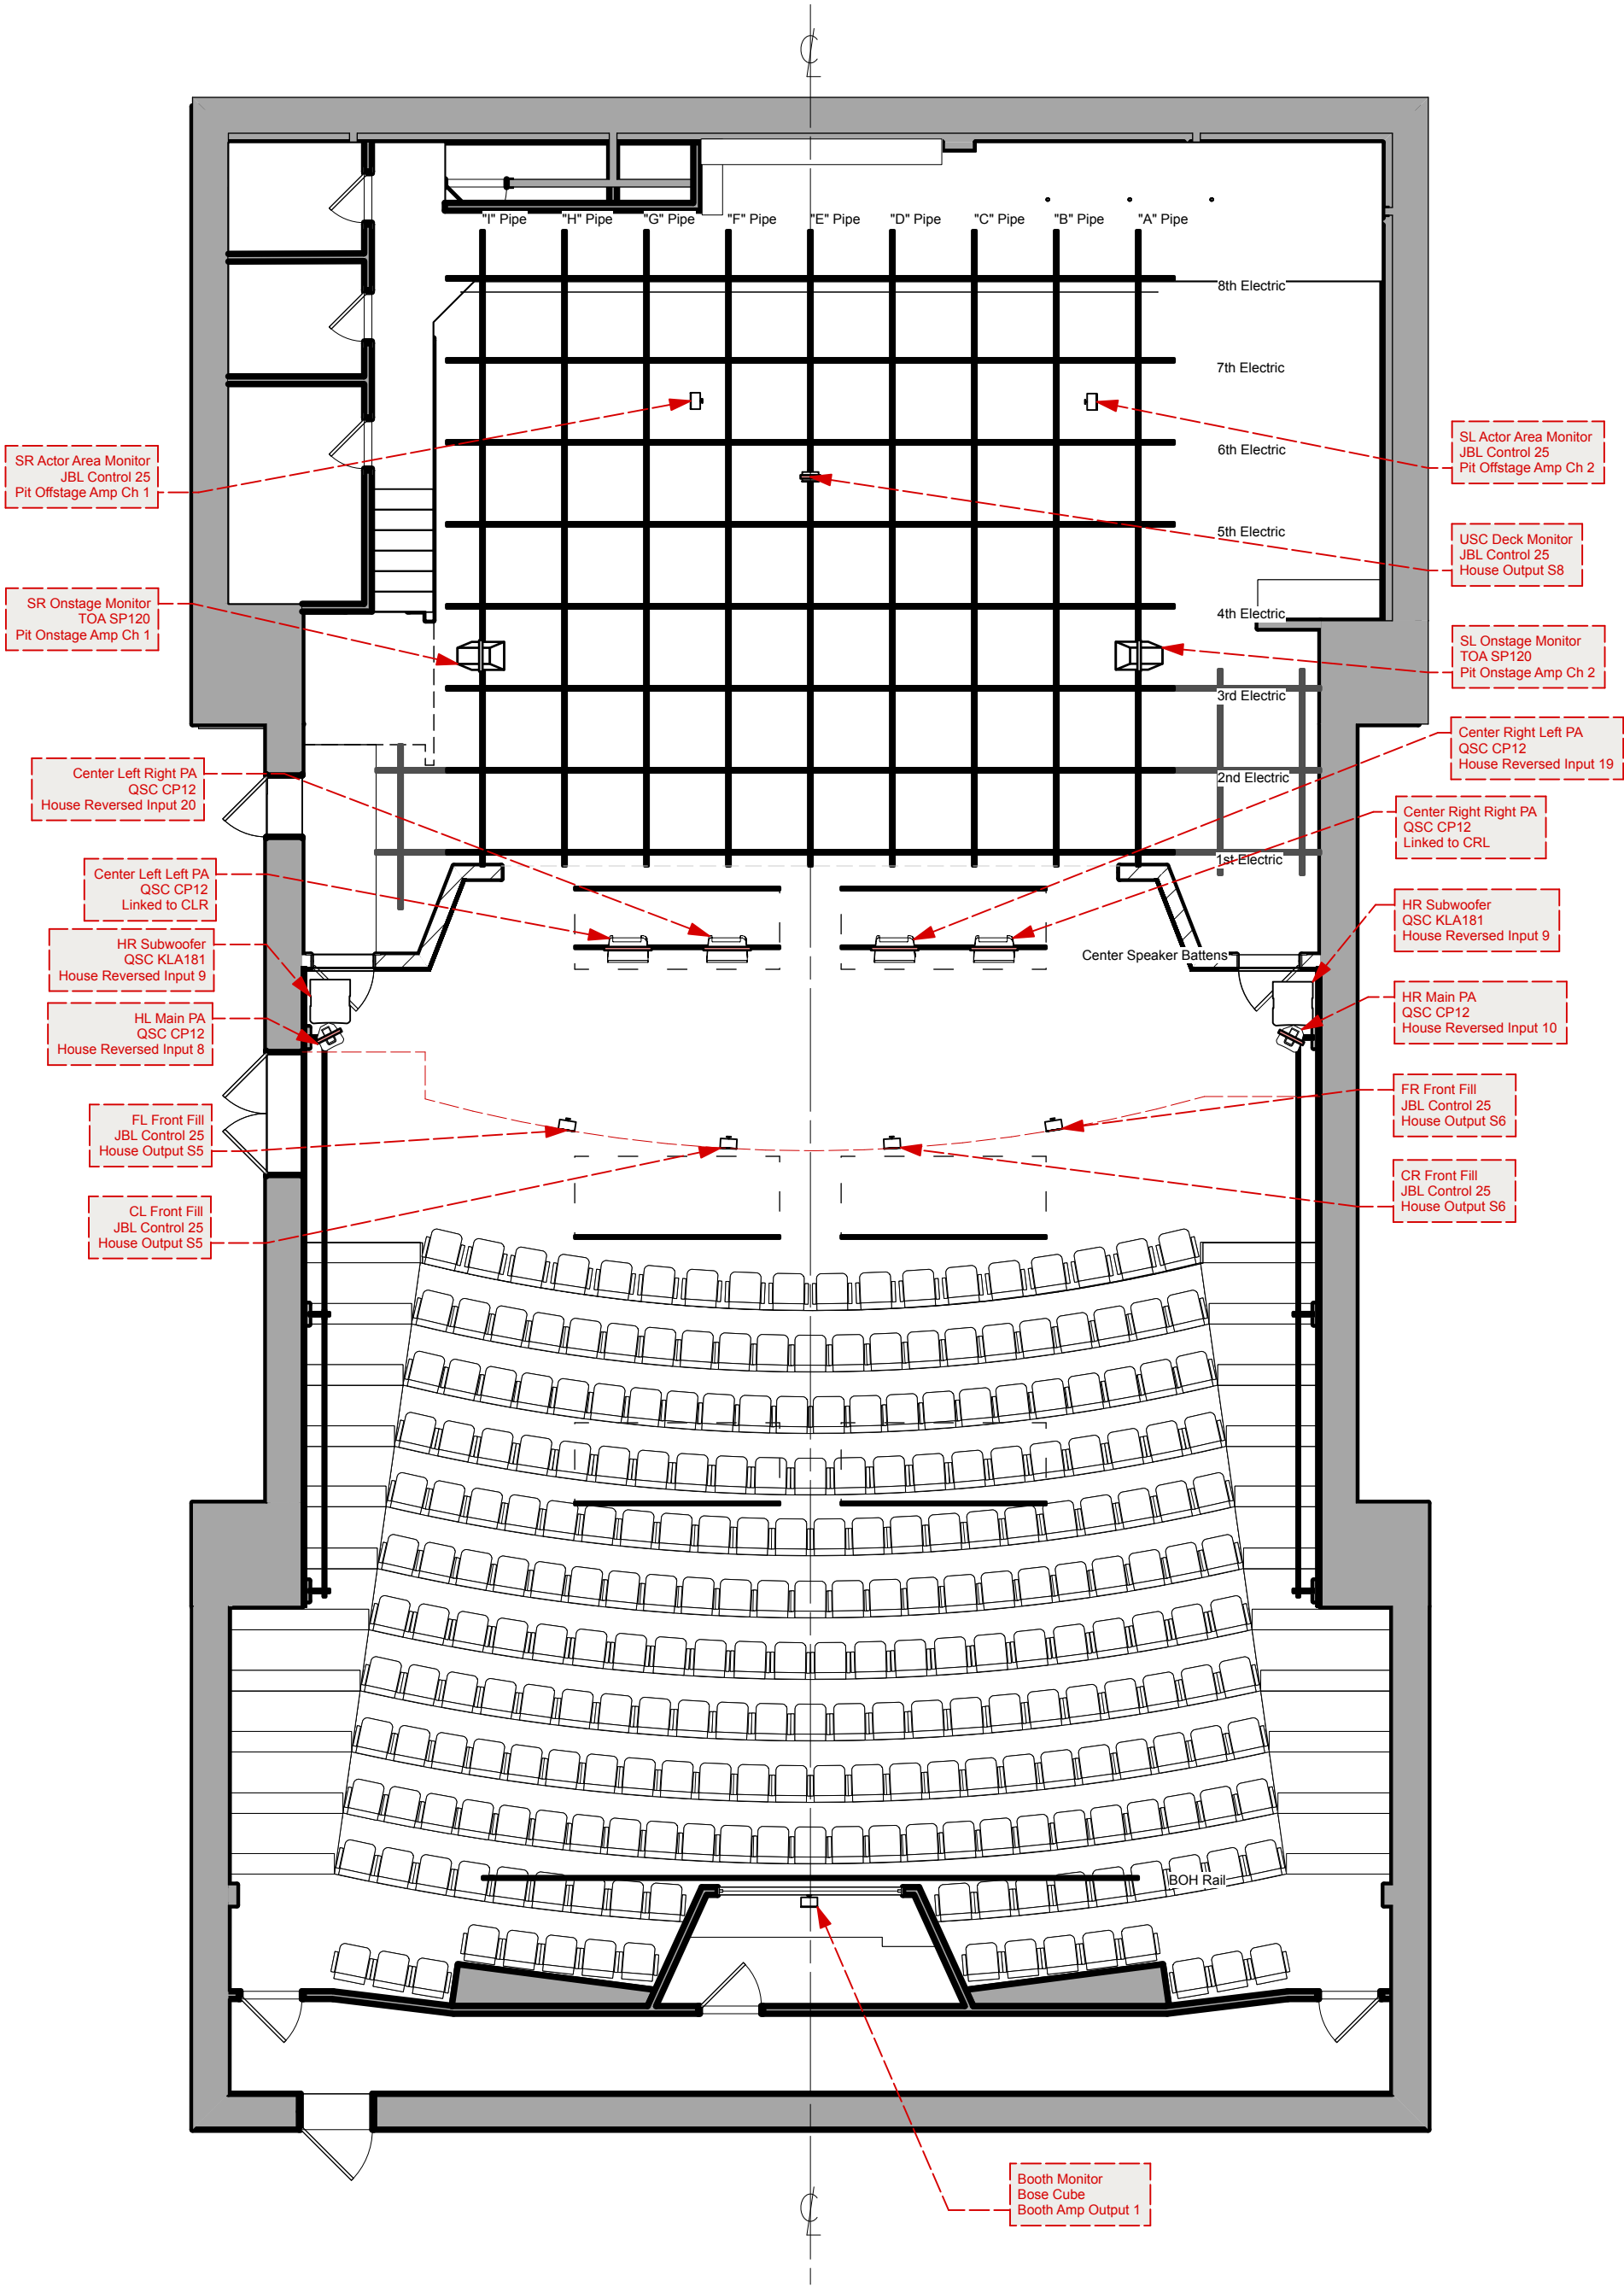

GEORGE FOX UNIVERSITY THEATRE - WOOD-MAR AUDITORIUM
"THE HUNCHBACK OF NOTRE DAME"

DIRECTOR: BEN TISELL
SOUND DESIGNER: TODD RYLAARSDAM

Speaker Plot

SCALE: SCALE: 1/8"=1'-0"
DATE: DATE:


PAPER SIZE: PAPER SIZE: 11 x 17

PLATE:

SP

These drawings represent design and conceptual information only. They do not address the structural or electrical appropriateness of the design's installation and realization. All applicable fire and safety codes are to be strictly applied.


VECTORWORKS EDUCATIONAL VERSION

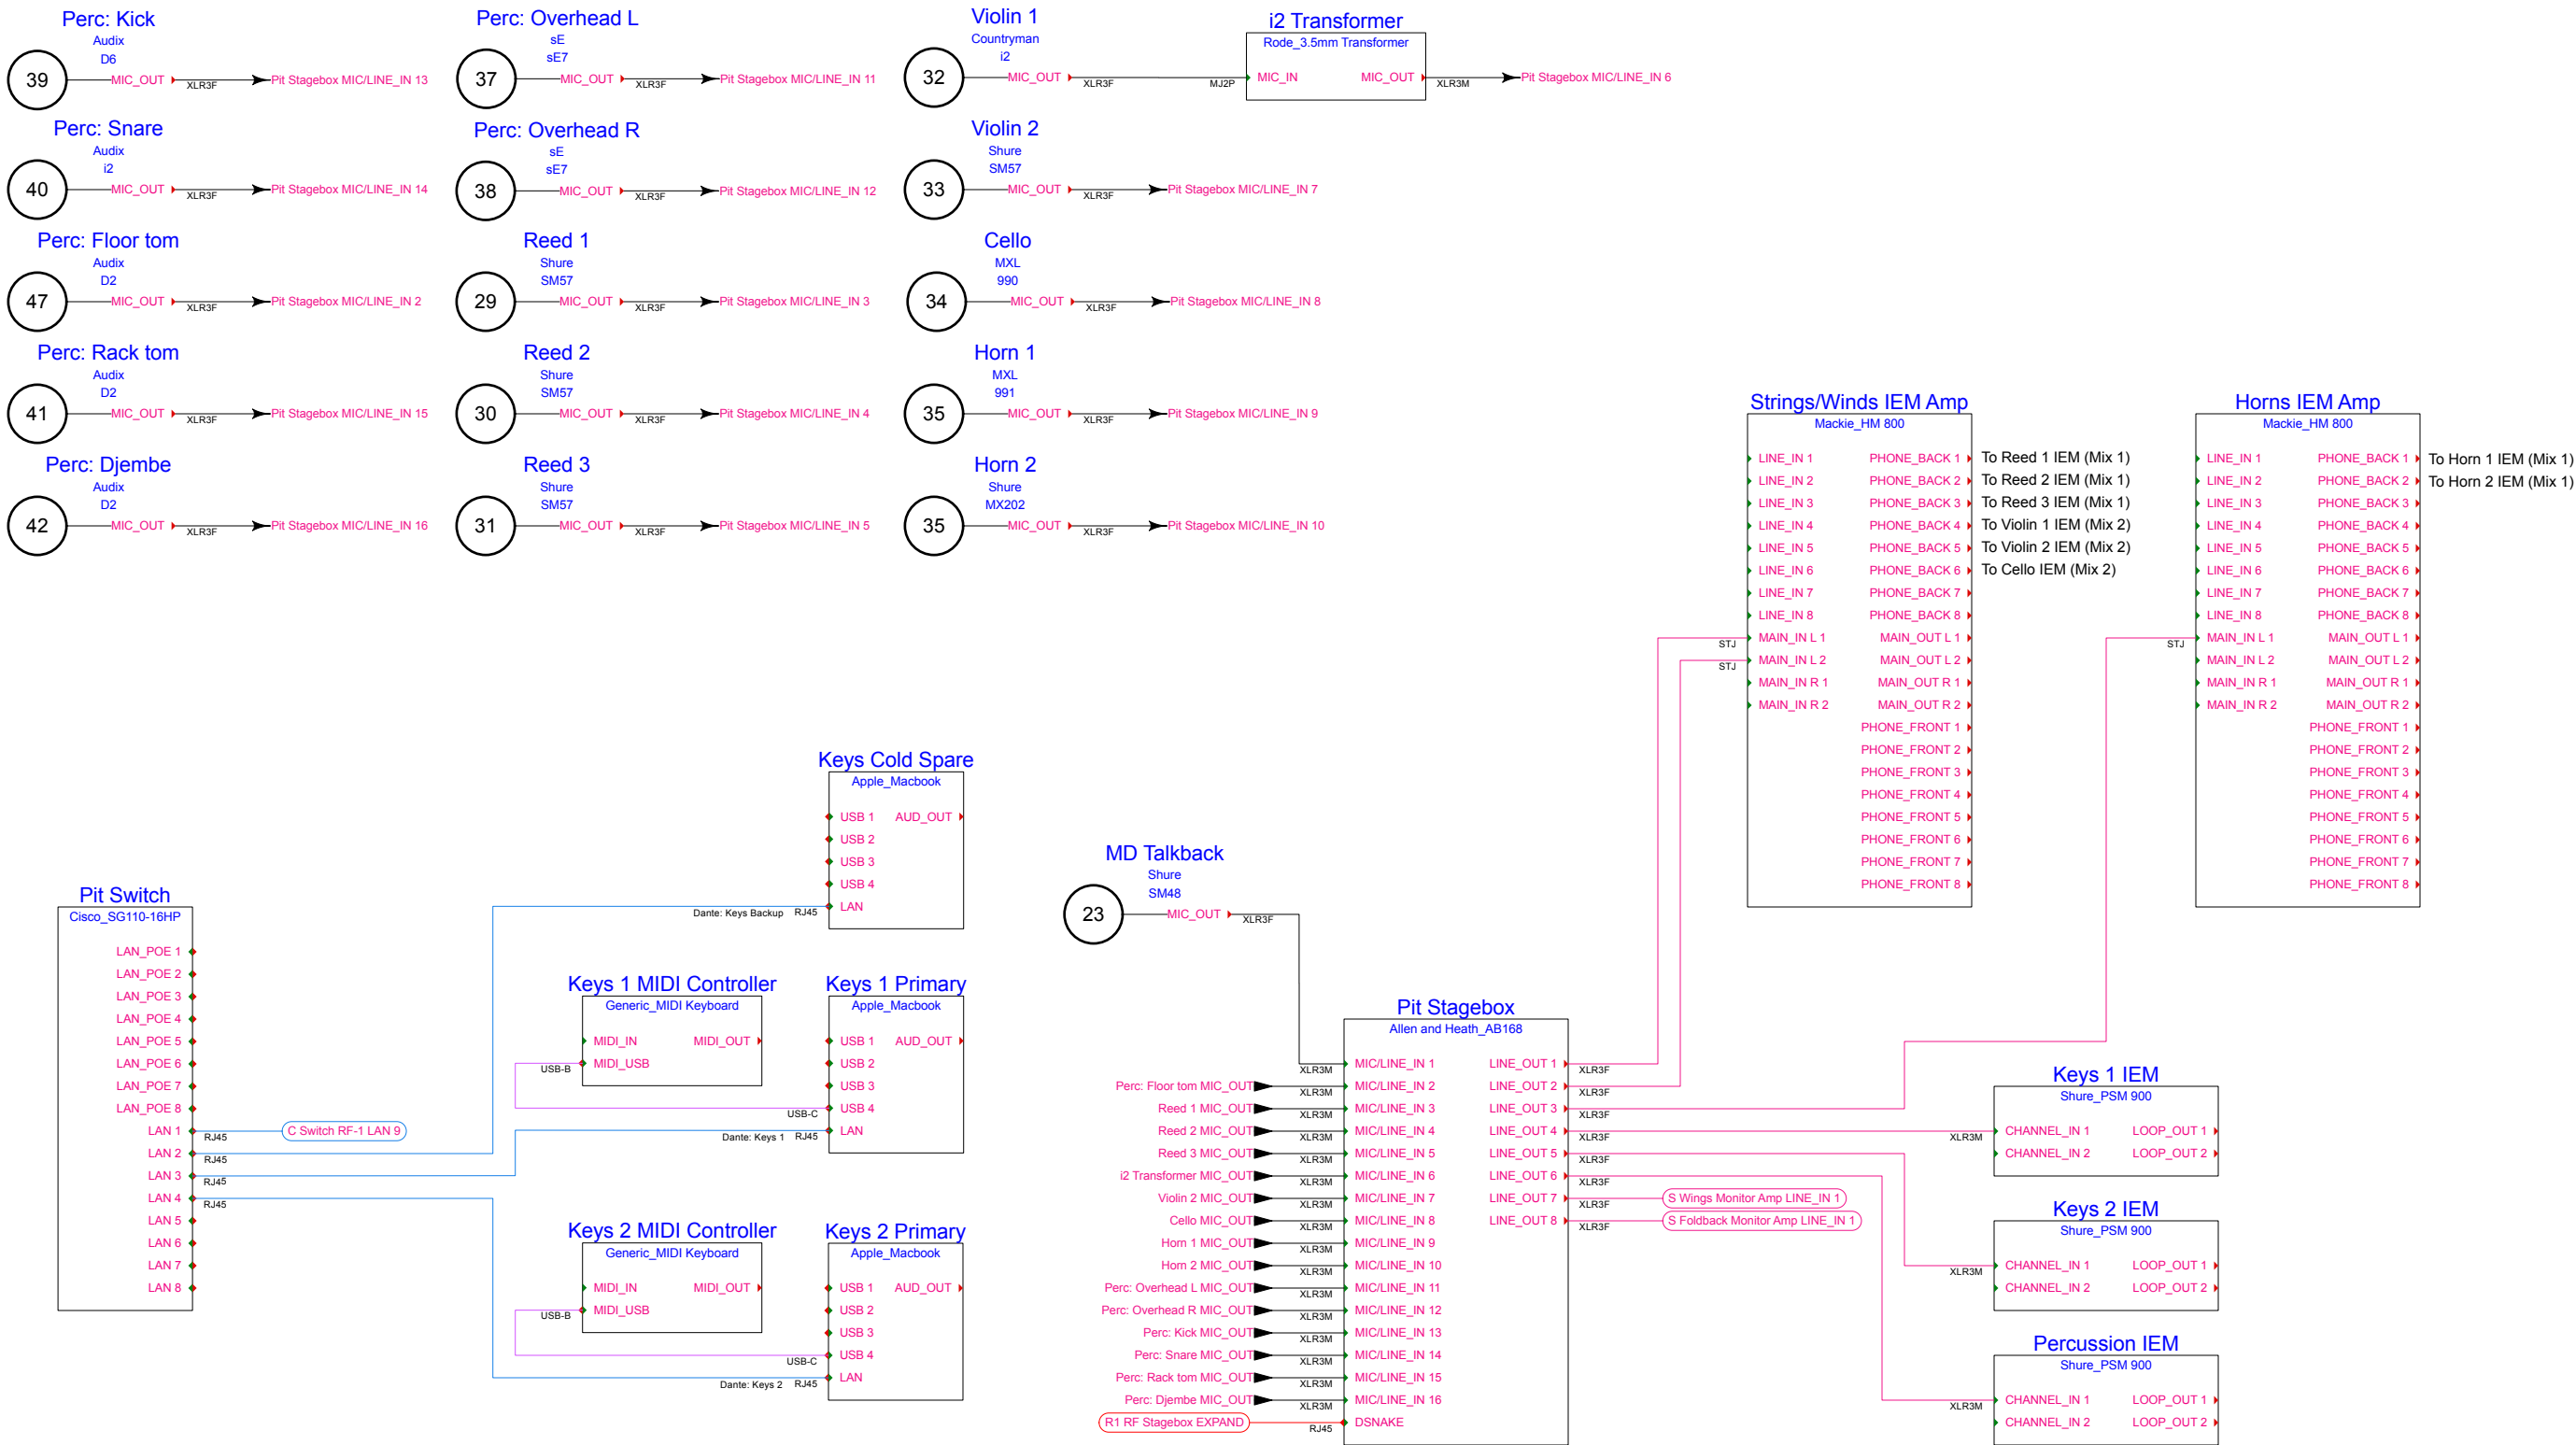

VECTORWORKS EDUCATIONAL VERSION

These drawings represent design and conceptual information only. They do not address the structural or electrical appropriateness of the design's installation and realization. All applicable fire and safety codes are to be strictly applied.

LEGEND	
RF CH A	
RF CH B	
MIC	
LAN	

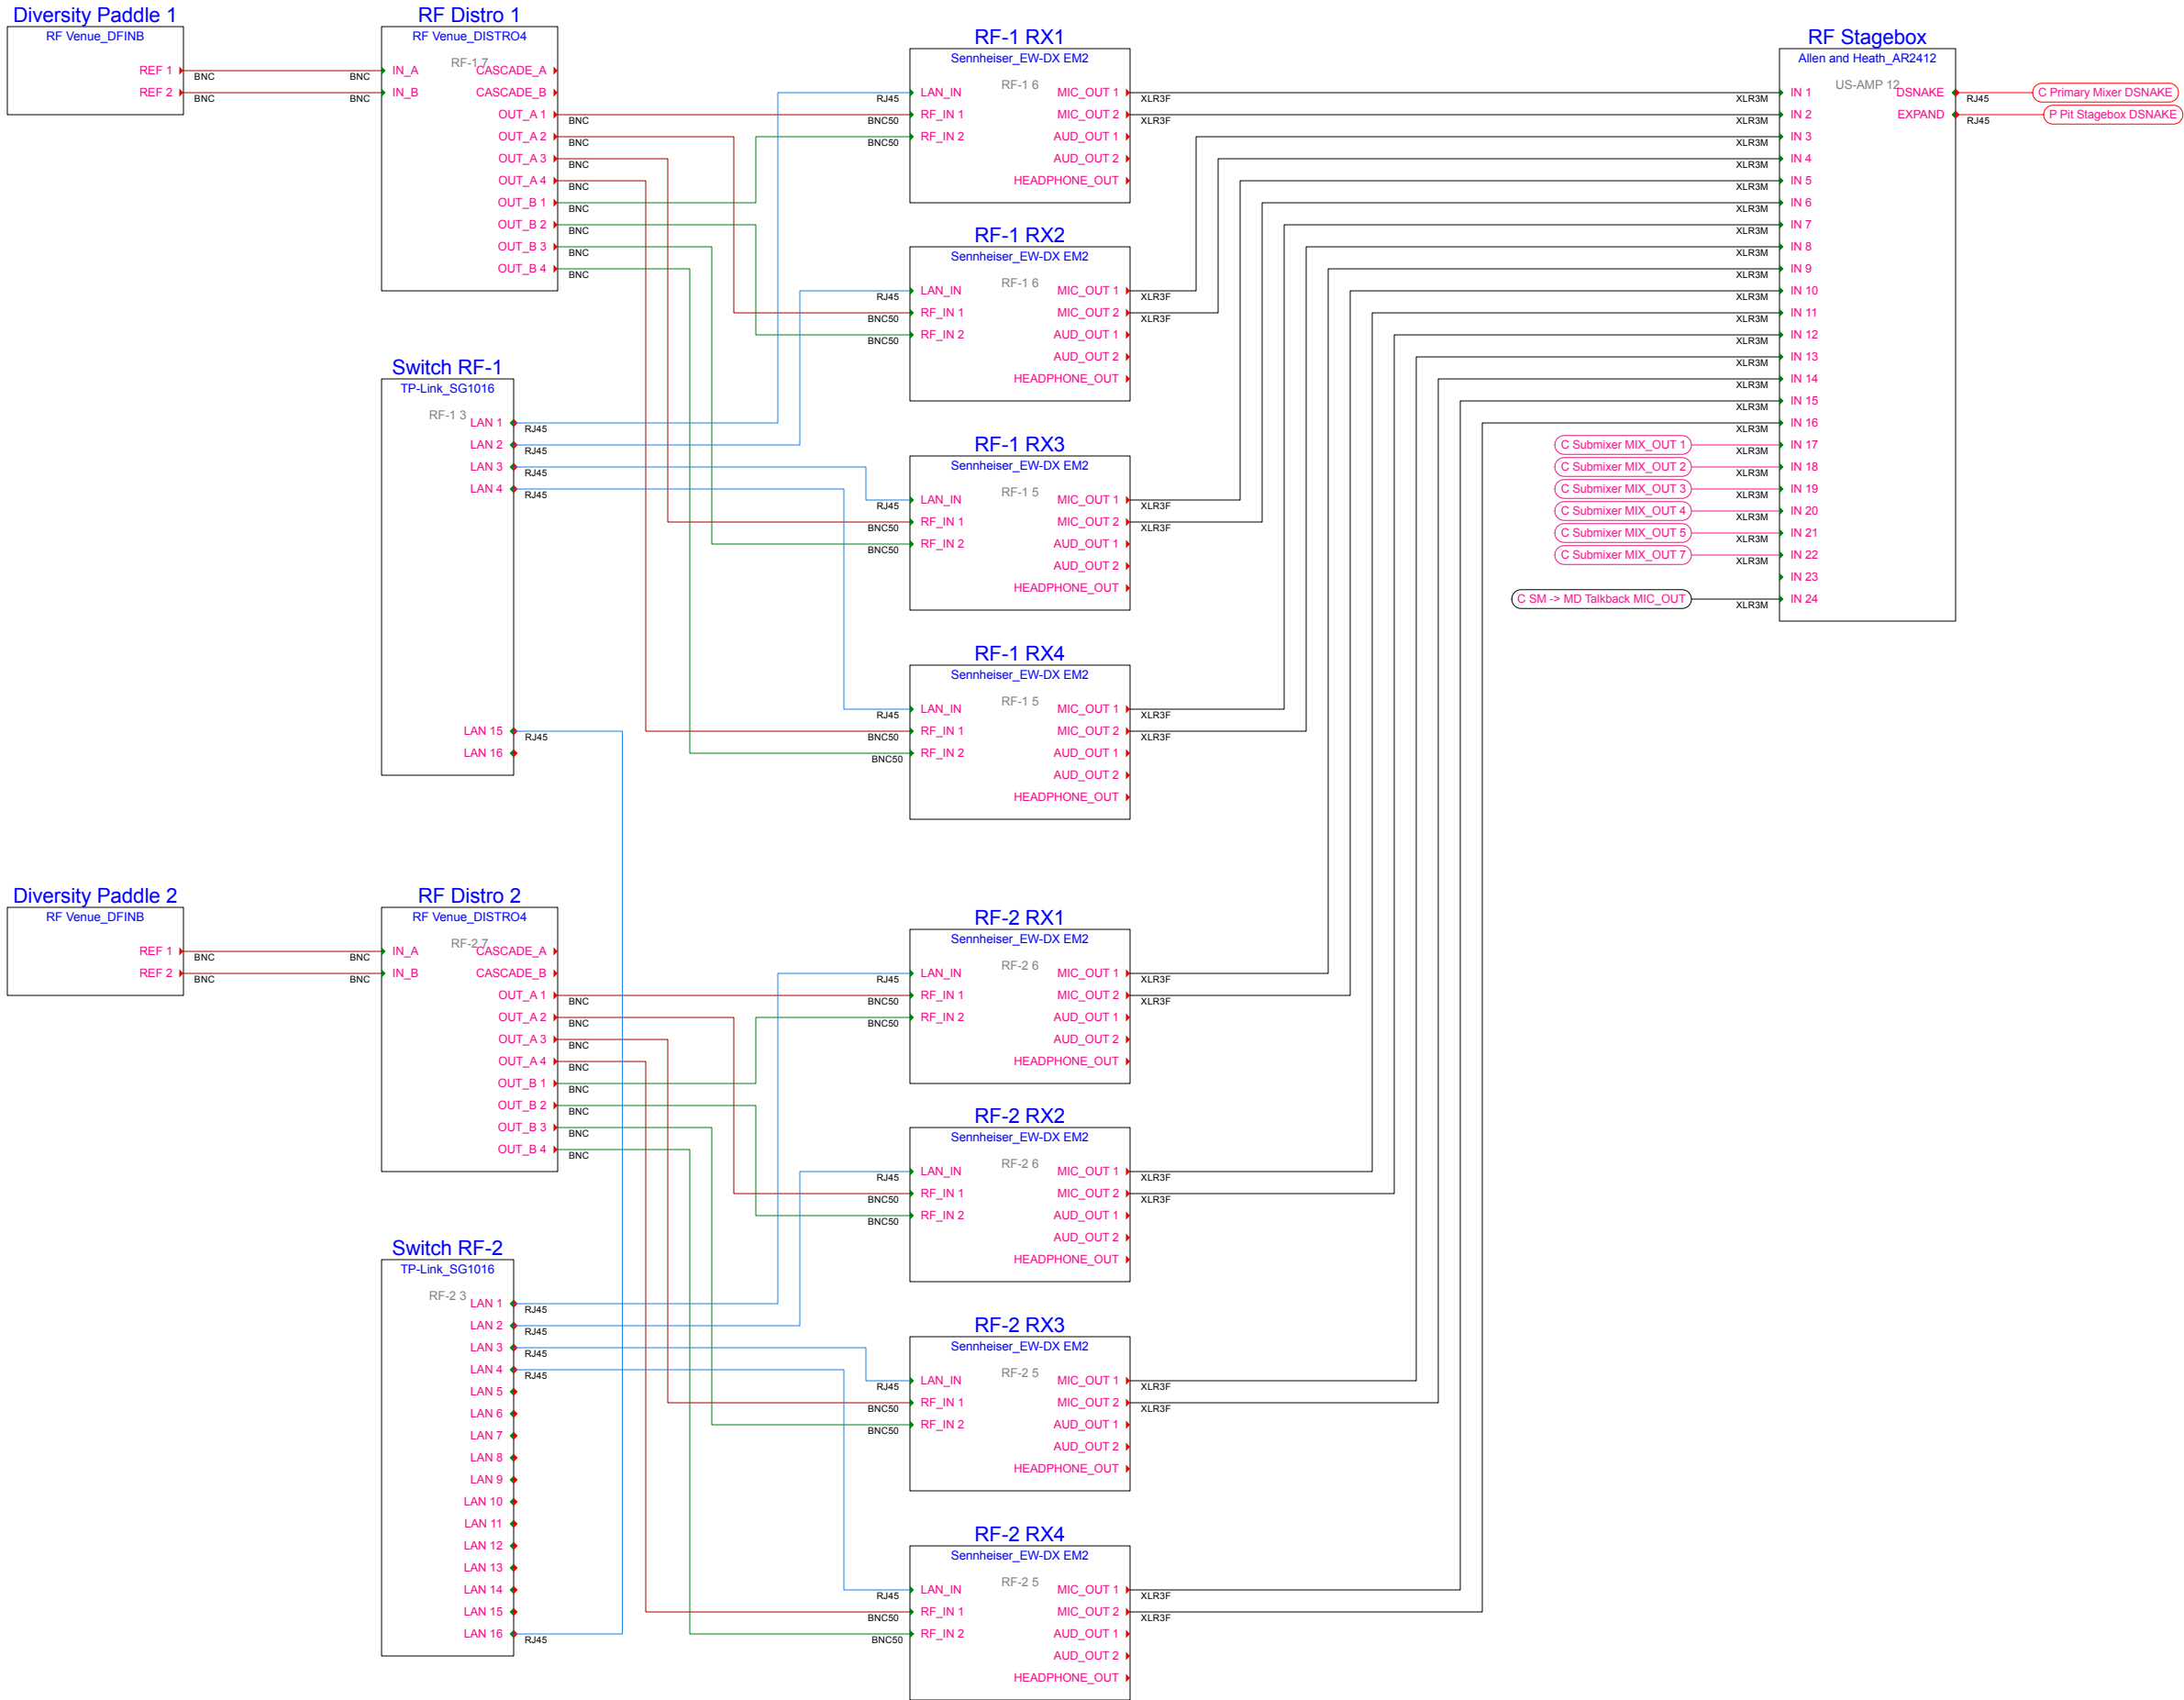

VECTORWORKS EDUCATIONAL VERSION

VECTORWORKS EDUCATIONAL VERSION

GEORGE FOX UNIVERSITY THEATRE - WOOD-MAR AUDITORIUM
"THE HUNCHBACK OF NOTRE DAME"

Digital RF (FOH)

PLATE:


R1



DIRECTOR: BEN TISSELL
SOUND DESIGNER: TODD RYLAARSDAM

SCALE:
DATE:
REV:
PAPER SIZE: 11" x 17"

These drawings represent design and conceptual information only. They do not address the structural or electrical appropriateness of the design's installation and realization. All applicable fire and safety codes are to be strictly applied.

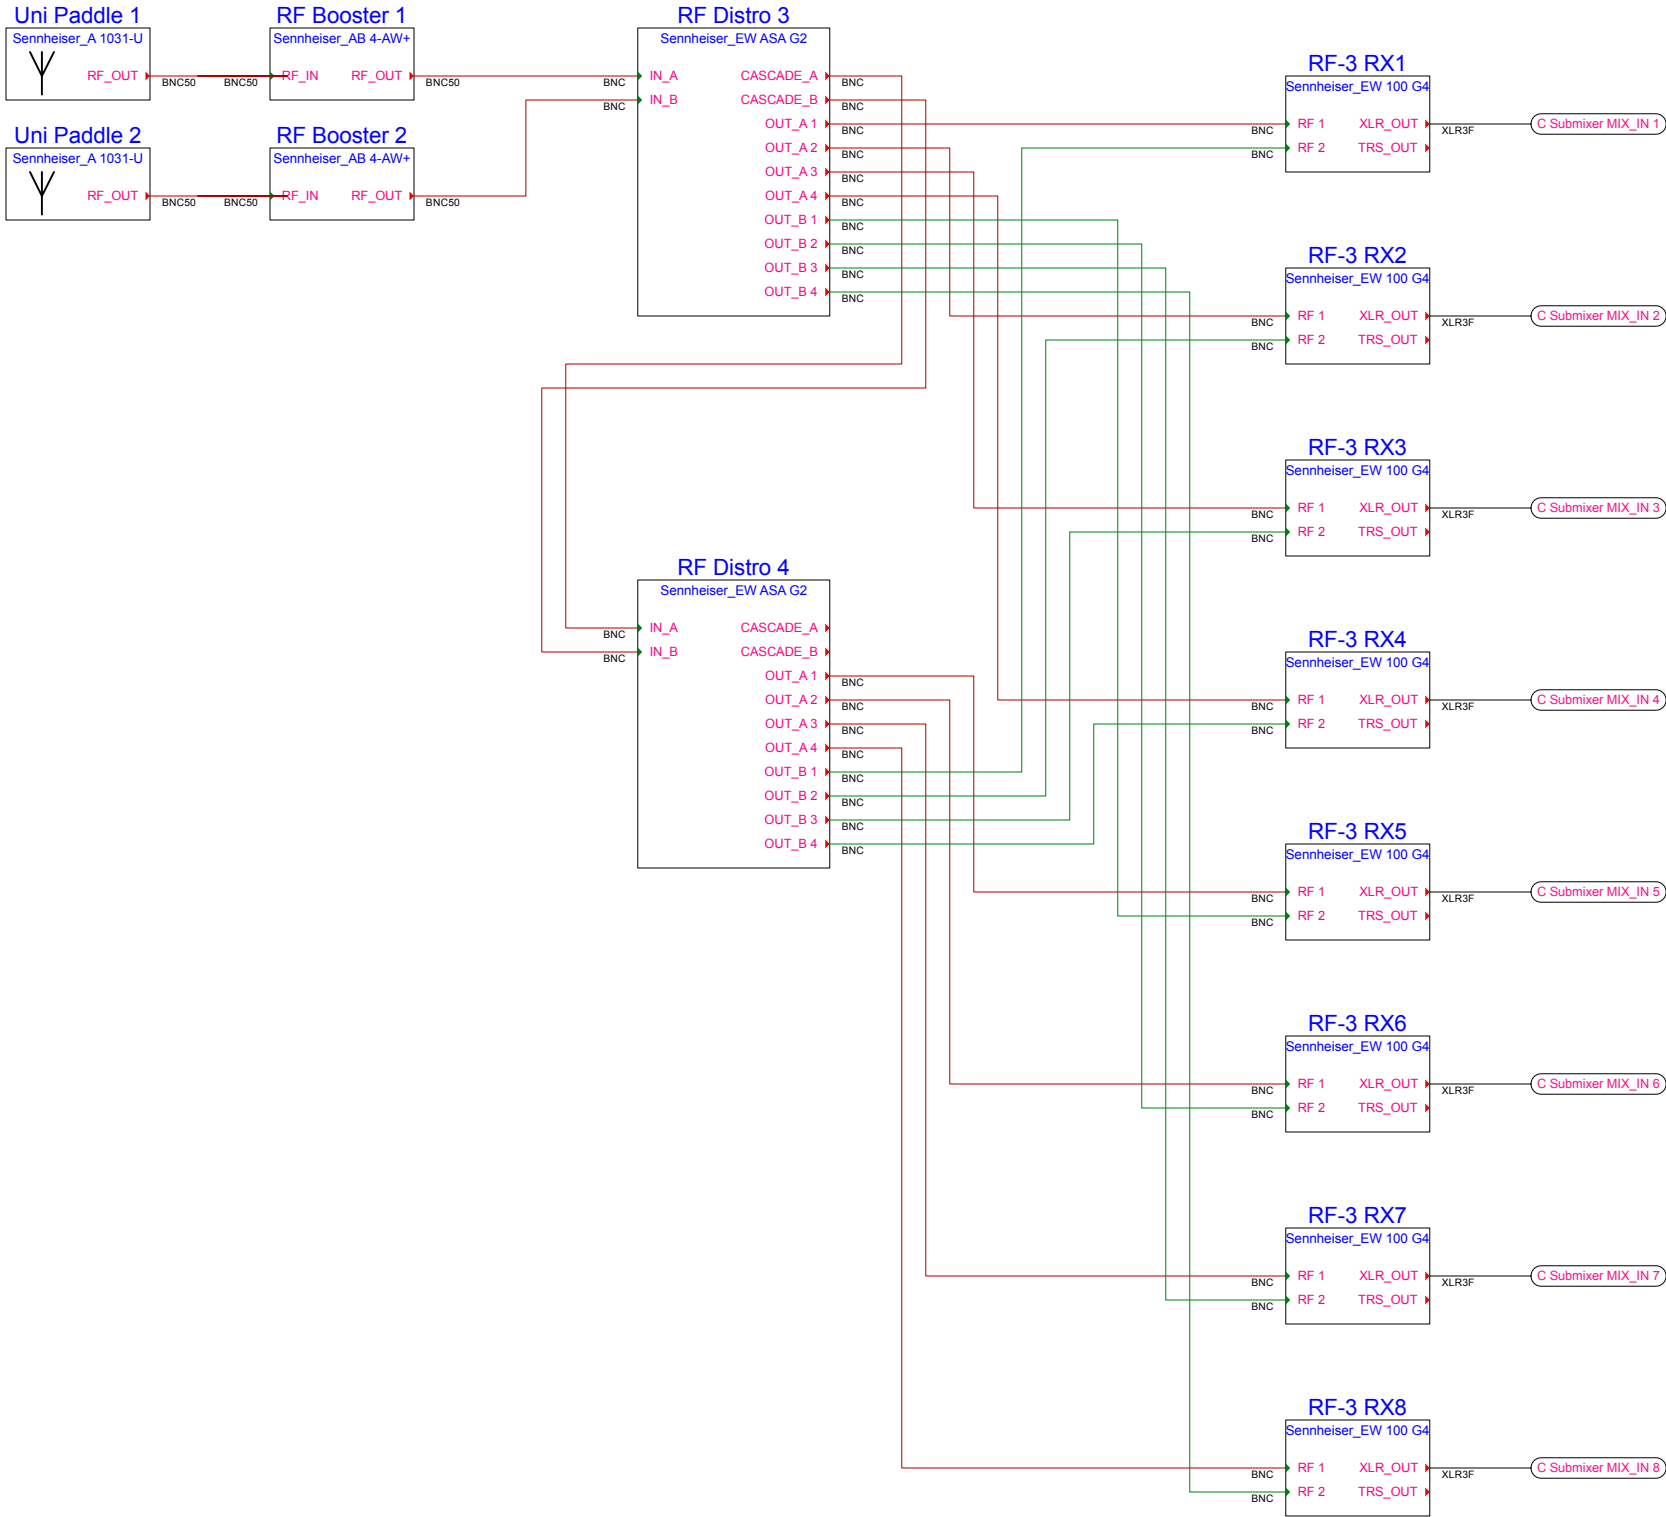

VECTORWORKS EDUCATIONAL VERSION

VECTORWORKS EDUCATIONAL VERSION



GEORGE FOX UNIVERSITY THEATRE - WOOD-MAR AUDITORIUM

"THE HUNCHBACK OF NOTRE DAME"

DIRECTOR: BEN TISSELL
SOUND DESIGNER: TODD RYLAARSDAM


Analog RF (FOH)

SCALE:
DATE:
REV:
PAPER SIZE: 11" x 17"

PLATE:

R2

These drawings represent design and conceptual information only. They do not address the structural or electrical appropriateness of the design's installation and realization. All applicable fire and safety codes are to be strictly applied.

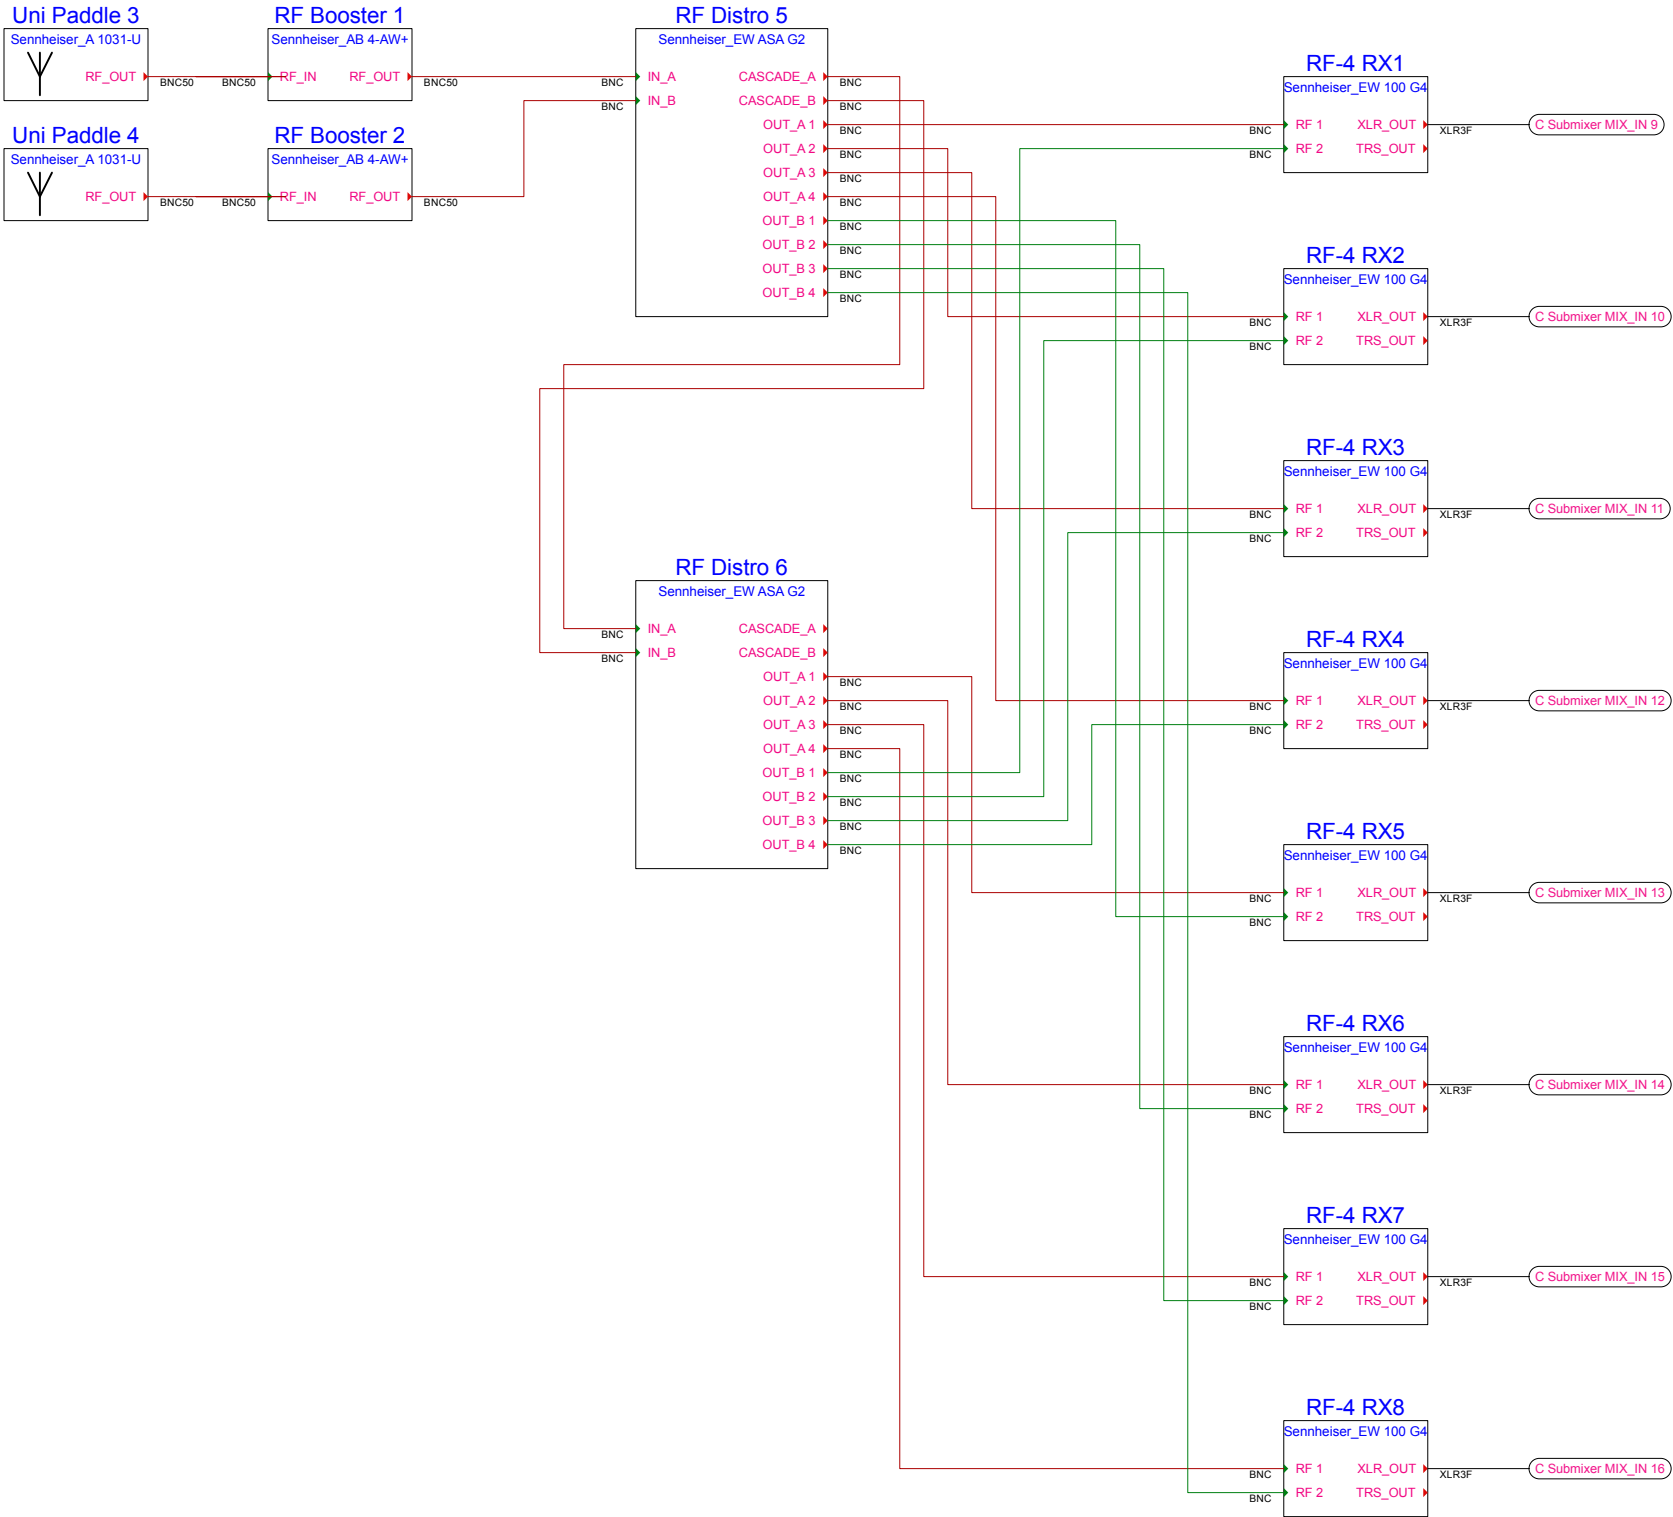

VECTORWORKS EDUCATIONAL VERSION

VECTORWORKS EDUCATIONAL VERSION



GEORGE FOX UNIVERSITY THEATRE - WOOD-MAR AUDITORIUM
"THE HUNCHBACK OF NOTRE DAME"

DIRECTOR: BEN TISSELL
SOUND DESIGNER: TODD RYLAARSDAM




Analog RF (FOH)

SCALE:
DATE:
REV:
PAPER SIZE: 11" x 17"

PLATE:
R3

These drawings represent design and conceptual information only. They do not address the structural or electrical appropriateness of the design's installation and realization. All applicable fire and safety codes are to be strictly applied.

VECTORWORKS EDUCATIONAL VERSION

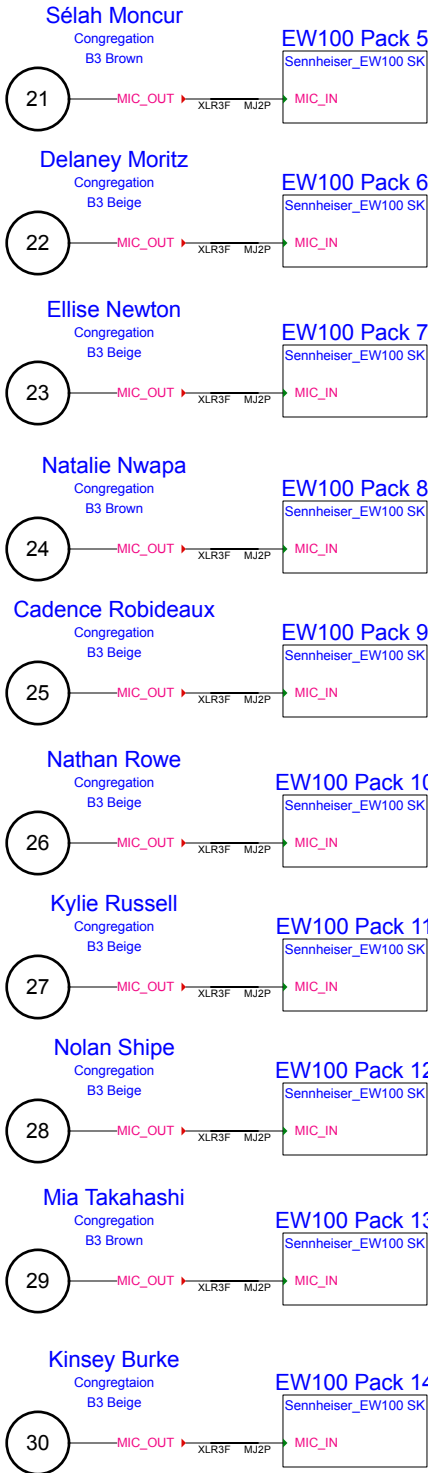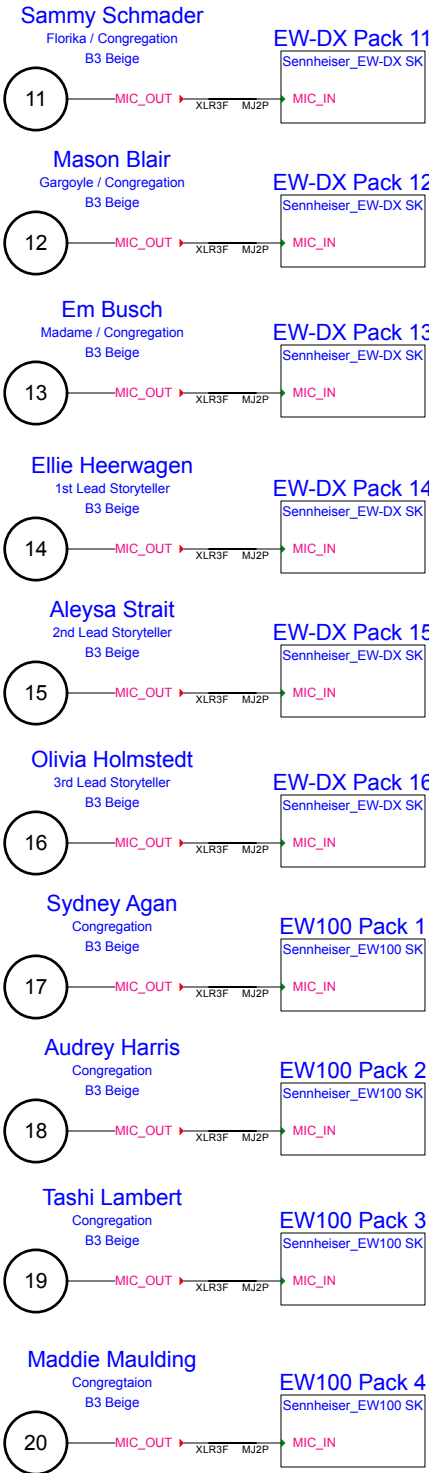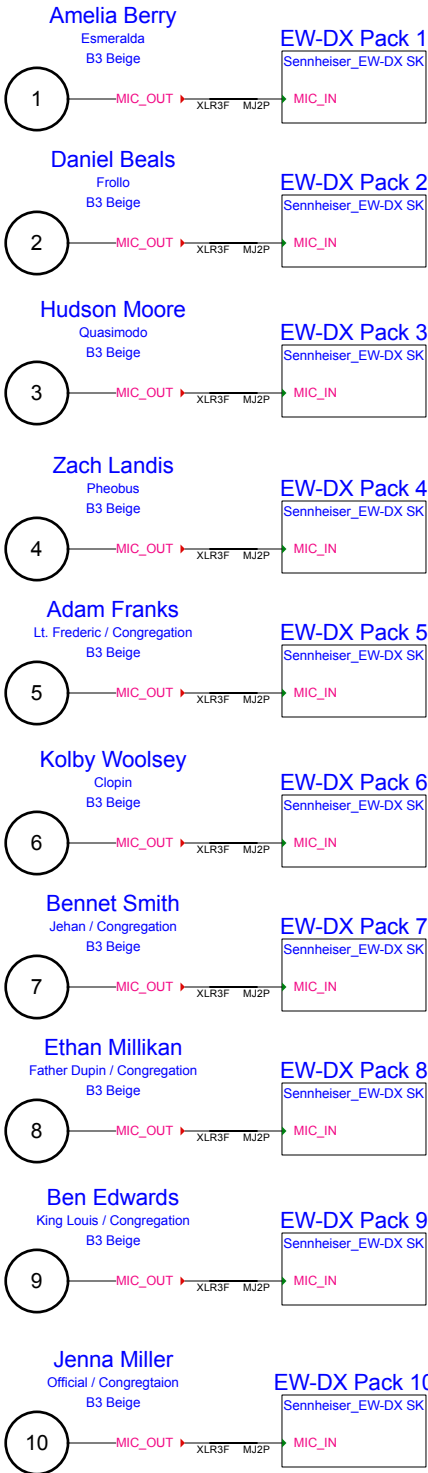

VECTORWORKS EDUCATIONAL VERSION



PLATE:

Actor Microphones

GEORGE FOX UNIVERSITY THEATRE - WOOD-MAR AUDITORIUM

"THE HUNCHBACK OF NOTRE DAME"



SCALE:
DATE:
REV:
PAPER SIZE: 11" x 17"

DIRECTOR: BEN TISSELL
SOUND DESIGNER: TODD RYLAARSDAM

These drawings represent design and conceptual information only. They do not address the structural or electrical appropriateness of the design's installation and realization. All applicable fire and safety codes are to be strictly applied.

